



260121時最新図
※Bodf(3)(7)(11)(15)については位置調整中(変更の可能性あり)

tR66-67間のBodwlには、別途工事によりブリーザーバルブ(200A用、150kg程度)を設置する。
キャリブレーションポートBrf×3のうち1箇所は別途工事によりブリーザーバルブ(17kg/1箇所)を設置する。

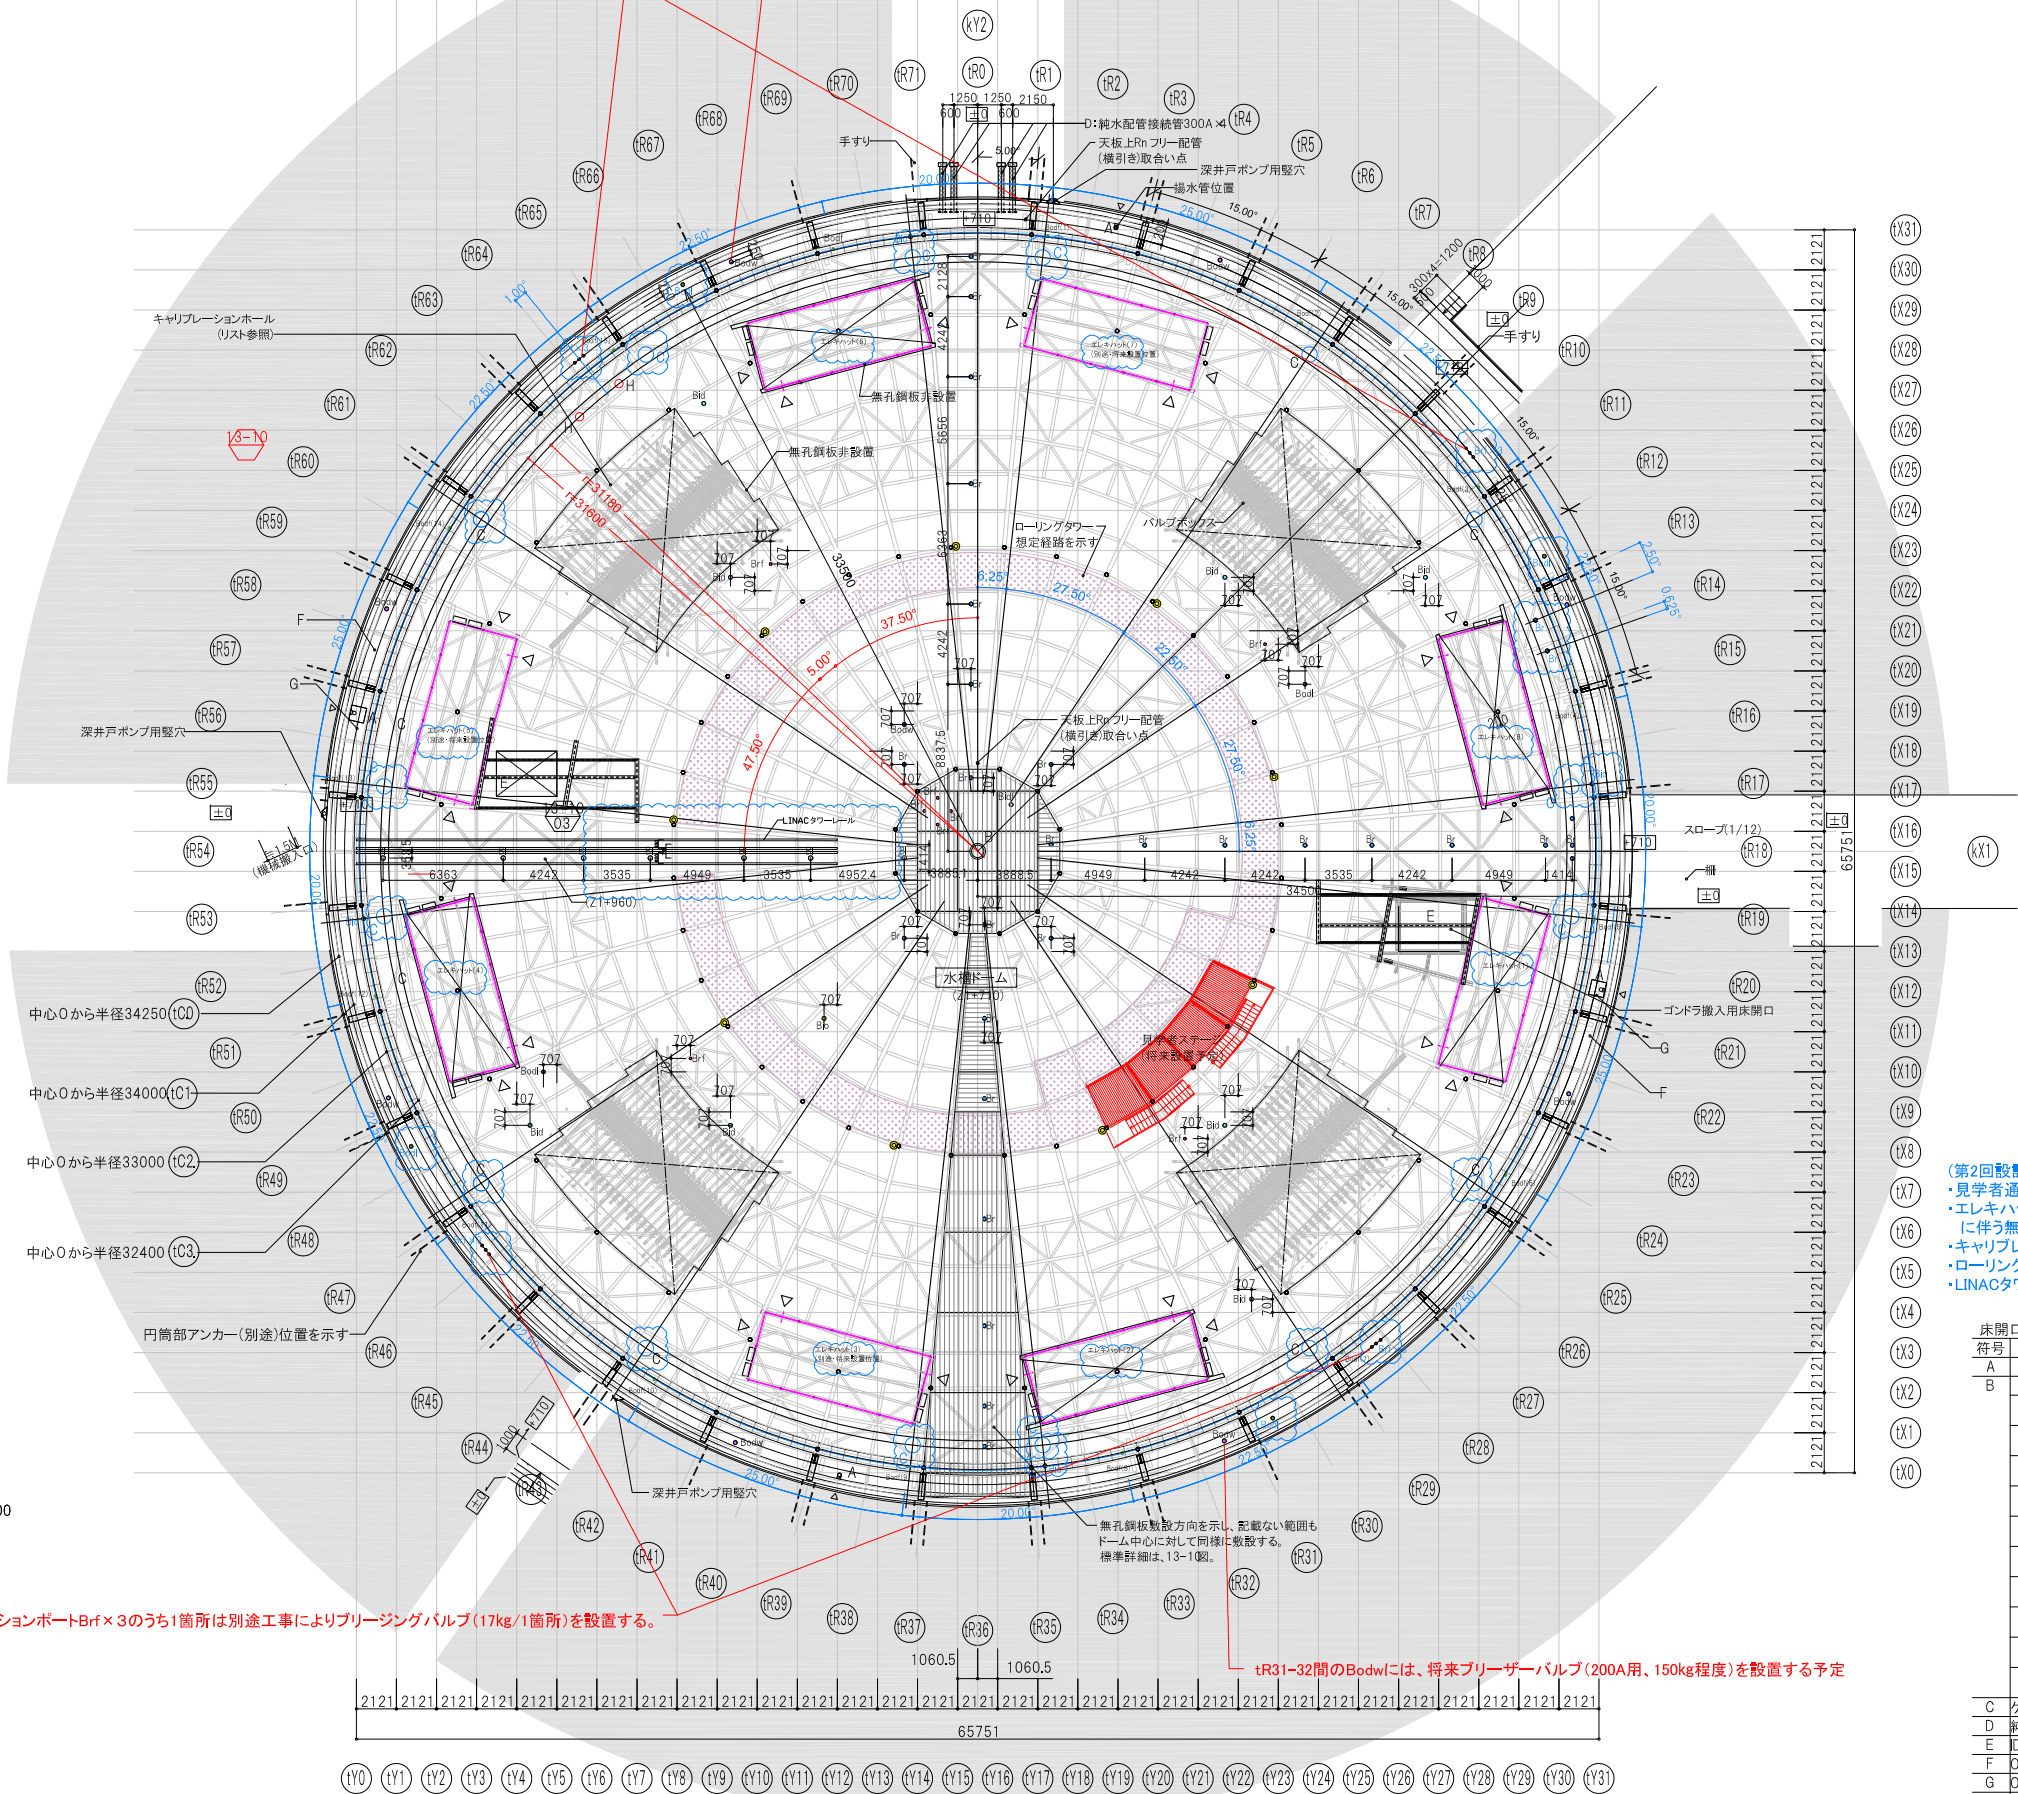

(第2回設計変更内容)
・見学者通路(将来対応)中止、見学者用ステージ(将来対応)追加
・エレキハット(別途工事)5か所追加、エレキハット(将来工事)3か所追加に伴う無孔鋼板非設置範囲の追加
・キャリブレーションポート(C、Bio、Bodf、Brf、Br(2か所))位置変更
・ローリングタワー想定経路図示
・LINACタワー用レール位置変更

床開口リスト			
符号	内容	サイズ	個所数
A	揚水管用	200A	計4か所
B	キャリブレーションホール		計103か所
●	Br Regular	200A	30か所
○	Bl LINAC	250A	7か所
●	Bodf OD (ファイバー用)	100A	16か所
●	Bodl OD (光源用)	200A	6か所
●	Bodw OD Water	200A	9か所
○	Bld ID Water	200A	8か所
○	Bldf ID (ファイバー用)	200A	1か所
○	Blo ID/OD Water	200A	5か所
■	Bc Center/Oversized	700□	1か所
●	Brf Rn free air	60φ (50A)	20か所
C	ケーブル取出孔	800φ	16か所
D	純水配管接続管(側部ライニング貫通管)	300A	計4か所
E	ID搬入用床開口	2000×300軽度	計2か所
F	ODゴンドラ点検口	800×2400	計2か所
G	OD点検口	800□	計2か所
H	地磁気補償コイル給電口	450φ	計2か所

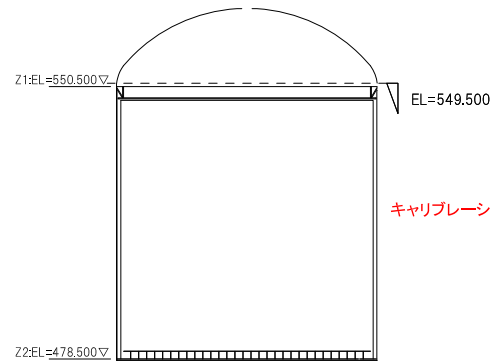

キャリブレーションポートBrf×3のうち1箇所は別途工事によりブリージングバルブ(17kg/1箇所)を設置する。

特記事項		凡例		日建設計		業務名称		工事名称		東京大学 施設部	
240610入札用図書		H○		Fs		東京大学（岐阜県神岡）ハイパーカミオカンデ（水槽及びPMT支持架構等）設計業務		東京大学（岐阜県神岡）ハイパーカミオカンデ（水槽及びPMT支持架構等）工事		東京大学 施設部	
訂正		鉄骨柱		転落・衝突防止柵		東京大学（岐阜県神岡）ハイパーカミオカンデ（水槽及びPMT支持架構等）設計業務		東京大学（岐阜県神岡）ハイパーカミオカンデ（水槽及びPMT支持架構等）工事		部長 計画課	
26.10.29 第2回設計変更		（+）		Hcst1.溶融鉛詰めつき/酸処理		東京大学（岐阜県神岡）ハイパーカミオカンデ（水槽及びPMT支持架構等）設計業務		東京大学（岐阜県神岡）ハイパーカミオカンデ（水槽及びPMT支持架構等）工事		関 沼尻 齋藤 本田 鎌田 西川	
		鉄筋コンクリート				チーフ 記名：河野 信		東京大学（岐阜県神岡）ハイパーカミオカンデ（水槽及びPMT支持架構等）工事		関 沼尻 齋藤 本田 鎌田 西川	
		底面導水溝（詳細：12-図による）				担当書記名：黒澤清高 村田朋子		東京大学（岐阜県神岡）ハイパーカミオカンデ（水槽及びPMT支持架構等）工事		関 沼尻 齋藤 本田 鎌田 西川	
		床点検口 Ya：歩行用防水型		タラップ		後 図 者：砂田 哲正		図面名称		作成年月	
		Yb：簡易密閉型		タラップ背かご付				水槽平面図(8) ドーム平面図		縮 尺	
										通し番号	
										A-21	
										図面番号	
										11 - 8	
										令和7年10月	
										1/200	
										1/400	